

クーリングタワー制御盤

電気図面

目 次

	ページ
制御盤	2～3
電気部品使用リスト	4
電源回路図	5～6
制御回路図	7～8
PLC入力回路	9～10
PLC出力回路	11～12

照 査

- ☐ 照査する
☒ 朱記訂正のうえ照査
☐ 朱記訂正のこと



株式会社 アドマテックス美濃

殿

図番名 クーリングタワー制御盤

有限会社 エイワ技電

項名称 目次 1

縮尺 1/10

設計

**

製図

**

検図



**

日付

26/06/09

頁

1 / 12

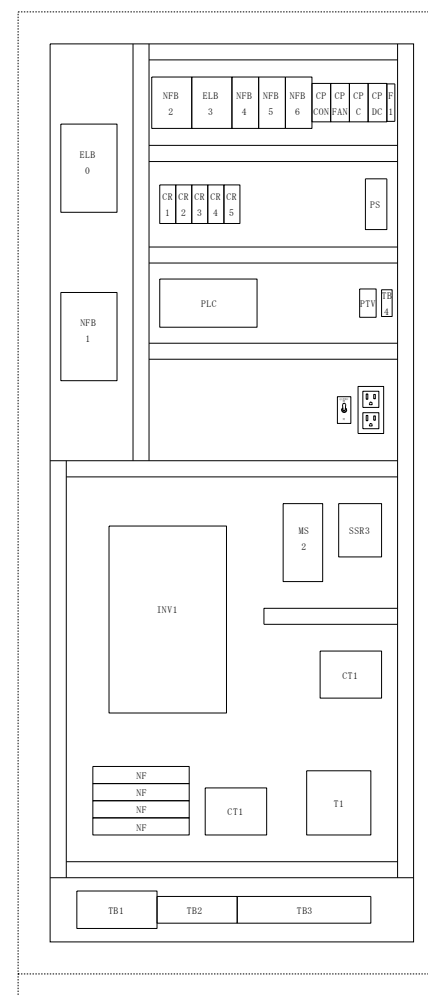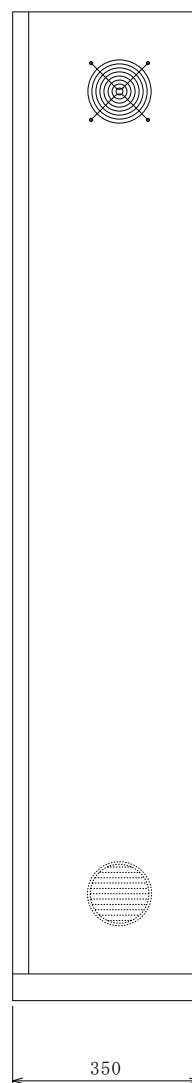

図番号	クーリングタワー制御盤	株式会社 アドマテックス美濃	設計	**	製図	**	検図	**	日付	26/06/09	頁	2 / 12
項名称	制御盤	有限会社 エイワ技電	縮尺 1/10									






落水防止弁？

薬注装置(水質管理装置)があるのならば(フロー図に記載なし)運転異常のランプがいるのでは？

フロー図に温度センサー表記無し。
ファン発停の表示？

制御電源	送水電動弁	送水ポンプ	クーリング*タリー	凍結防止ヒータ
ON	閉端	送水ポンプ停止	クーリング*タリー停止	凍結防止ヒータ停止
クーリング*ファン	送水電動弁動作異常	送水ポンプ過負荷	クーリング*タリー過負荷	凍結防止ヒータ高温異常

フロー図にヒーター記載なし。
冷却塔下部水槽にある？

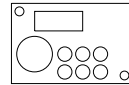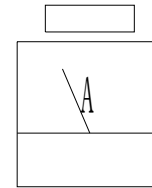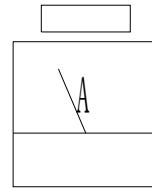


手動の切り替えがあるのに
手動操作用の釦無し？

積算電力計を設置してください。



扉を開けても動力遮断されないことの表示

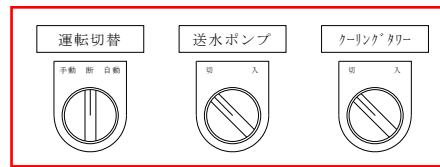

自動運転は、
どのような動き？



ブザー？

名 称	メーカー	型 式	容 量	数 量	備 考	名 称	メーカー	型 式	容 量	数 量	備 考
制御盤	日 東	R35-818B		1		集合表示灯	IDEC	SCL30N-0305		1	
漏電ﾌﾟﾚｰｶ	三 菱	NV250CV	3P150A 100～500mA	1	カバー付	表示灯	富士電機	DR30D0L-M3PW	AC200V	1	
ﾛｰﾋｭｰｽﾞﾌﾟﾚｰｶ	三 菱	NF250CV	3P150A	1	カバー付	セレクトスイッチ	富士電機	AR30PR-210B		3	
ﾛｰﾋｭｰｽﾞﾌﾟﾚｰｶ	三 菱	NF30KC	3P30A	1	カバー付	セレクトスイッチ	富士電機	AR30PR-311B		1	
漏電ﾌﾟﾚｰｶ	三 菱	NV30KC	3P30A 30mA	1	カバー付	電子報知器	ﾊﾞﾄﾗｲﾄ	BM-210H	AC100V	1	
ﾛｰﾋｭｰｽﾞﾌﾟﾚｰｶ	三 菱	NF30KC	2P5A	3	カバー付						
サーキットﾌﾞﾚｰｷ	三 菱	CP30BA	2P3A	1							
サーキットﾌﾞﾚｰｷ	三 菱	CP30BA	2P2A	2							
ﾋｭｰｽﾞ台	ｷﾑﾗ電機	F-10BS		1							
ｲﾝﾊﾞｰﾀ	三 菱	FR-F820-22K-1		1	22Kw用						
ﾛｲｽﾌｨﾙﾀｰ	三 菱	FR-BLF		4							
盤用換気扇	日 東	PF-091C-2		1							
ﾙｰﾊﾞｰ	日 東	LP-3		1							
可変式温度調節器	日 東	PTV-M61A		1							
電磁開閉器	富士電機	SW5-1	AC100V	3	3.7Kw用						
変流器	三 菱	CW-5L	100/5A	1							
変流器	三 菱	CW-5L	60/5A	1							
交流電流計	三 菱	YS206NAA-0-100A		1	3倍目盛り 赤指針						
交流電流計	三 菱	YS206NAA-0-20A		1	3倍目盛り 赤指針						
変圧器	ｽﾌﾞﾛｰ電機	SC21-500E	200/100V 500VA	1							
ソリッドステートコンタクト	オムロン	G3PE-215B-3N	DC24V	1							
ﾊﾞｰﾚｰﾌﾞﾗｲ	オムロン	S8VS-06024	2.5A	1							
シーケンサ	三 菱	FX3U-48MR/ES		1							

図番号

クーリングタワー制御盤

株式会社 アドマテックス美濃 殿

設計**

製図**

検図**


日付26/06/09


頁4 / 12

項名称

電気部品使用リスト

有限会社 エイワ技電

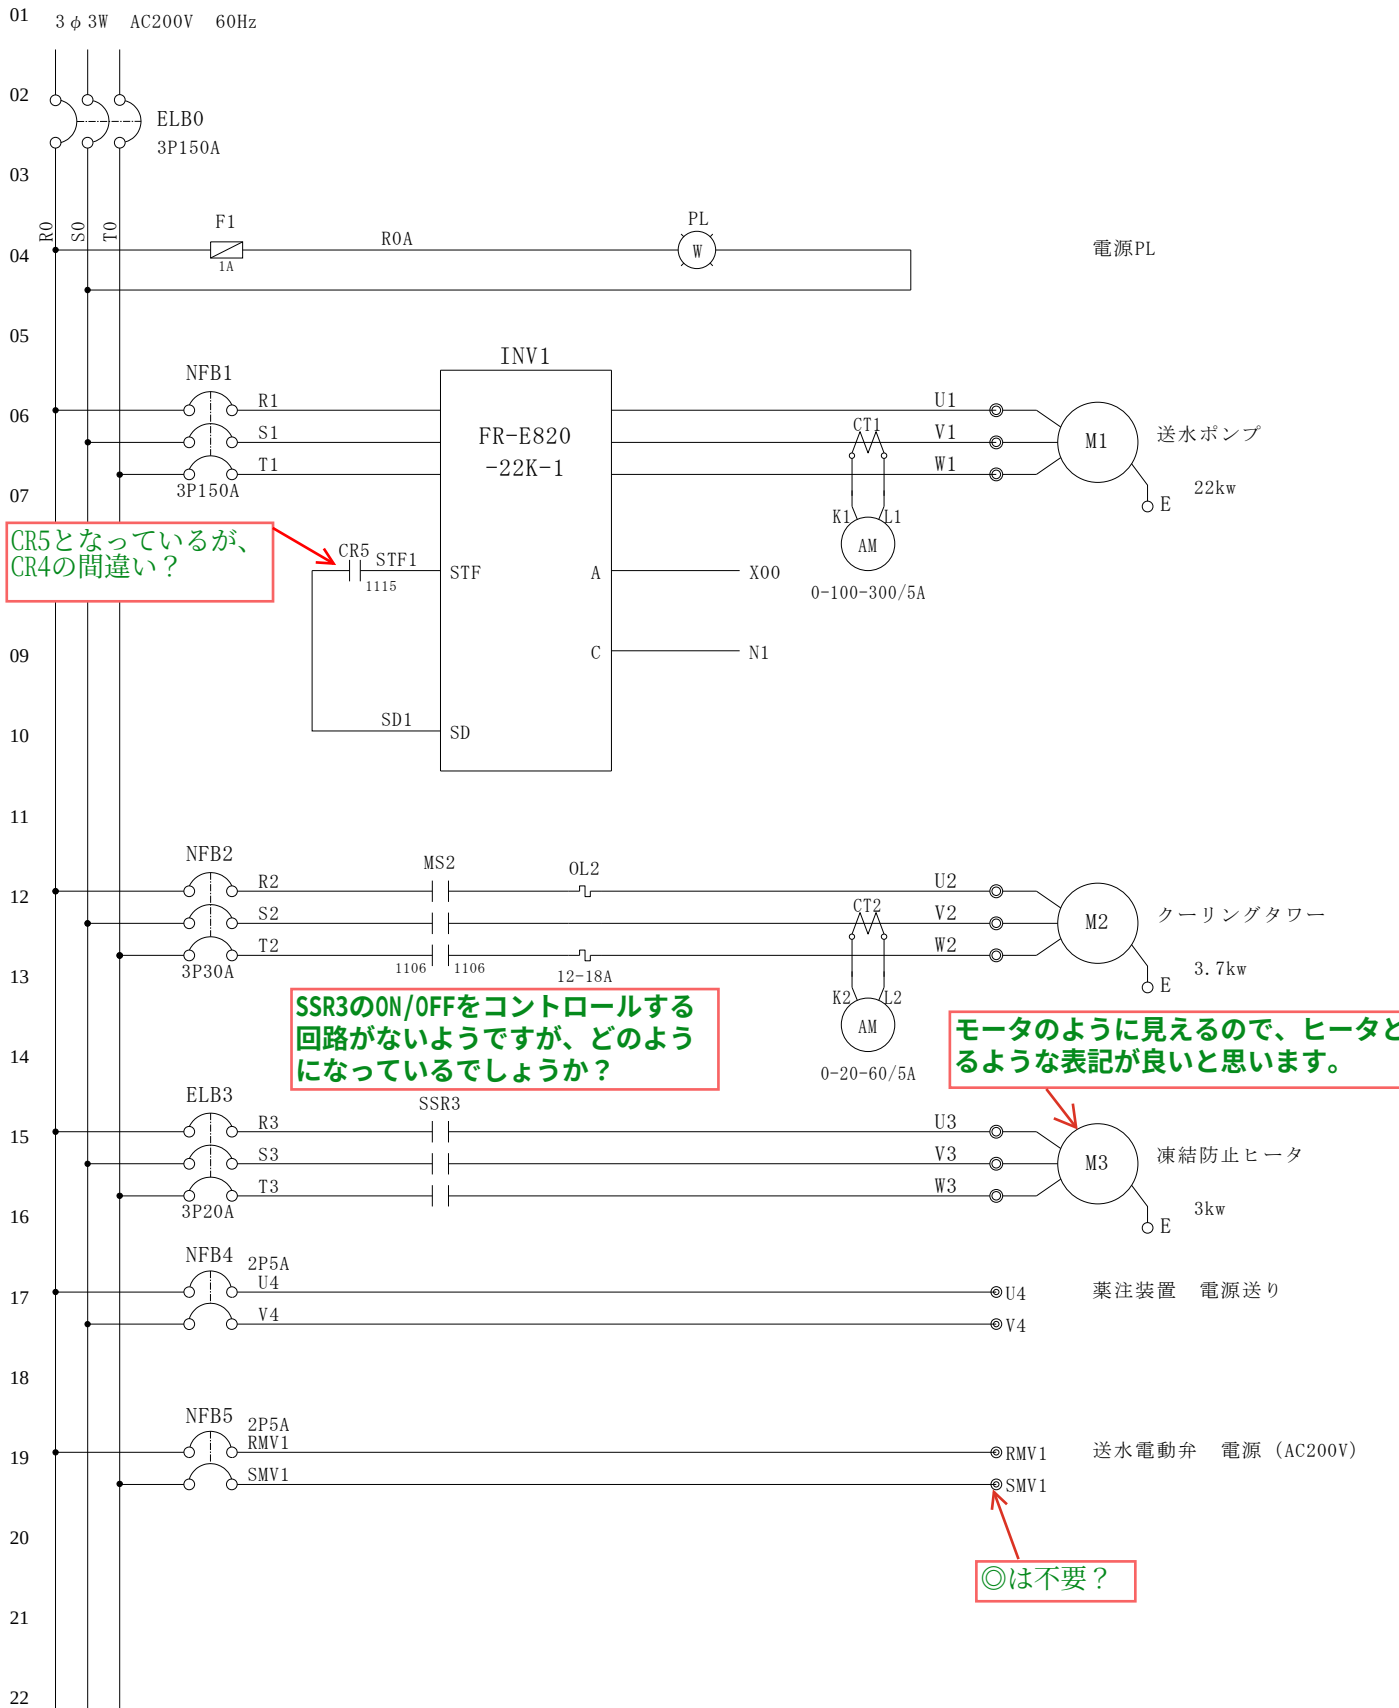[illegible]

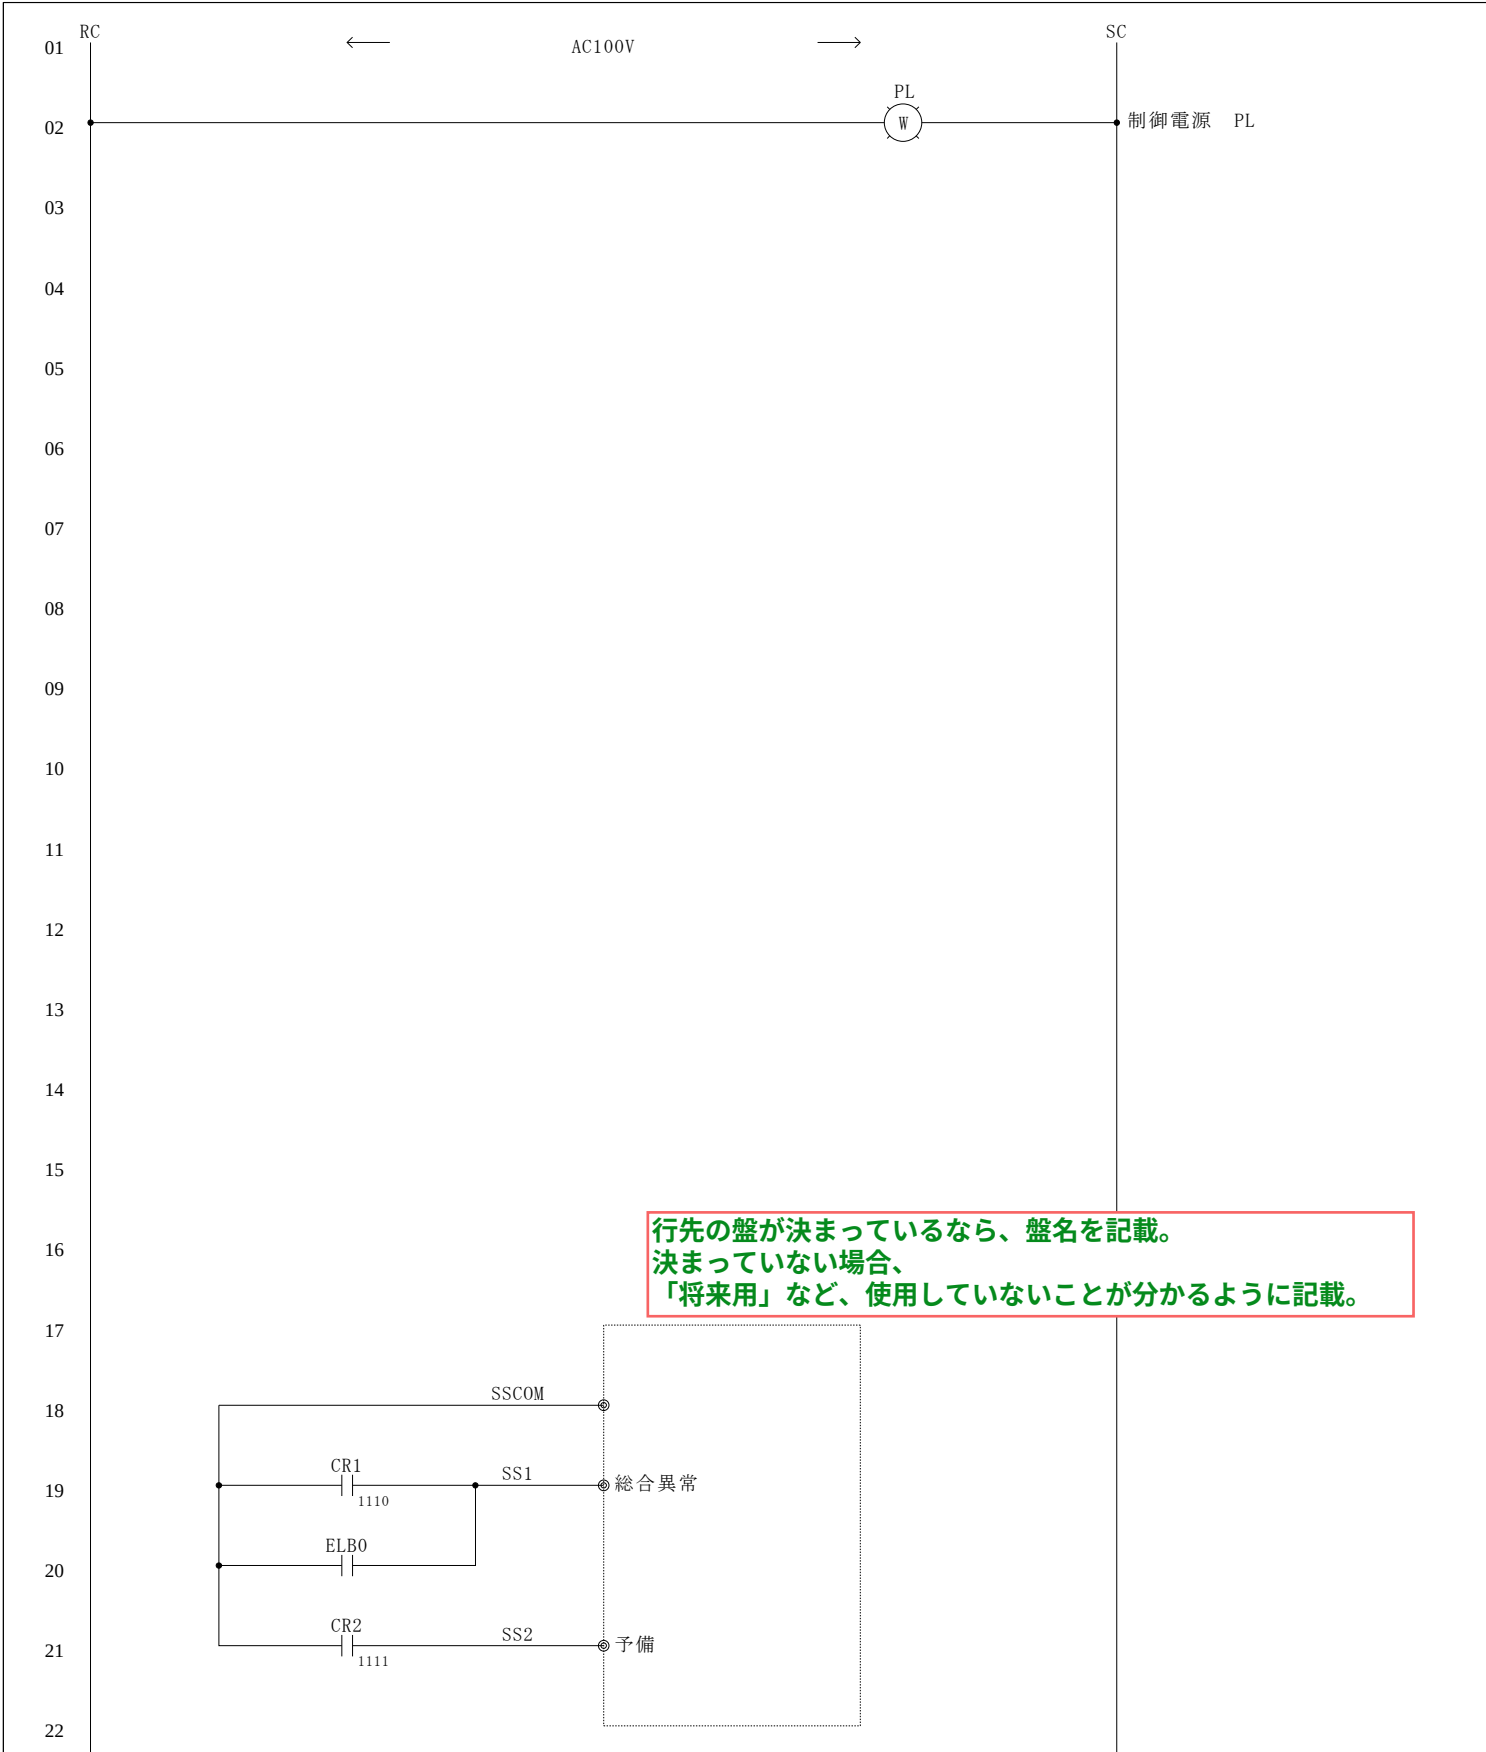

株式会社 アドマテックス美濃

殿

図番名

クーリングタワー制御盤

有限会社 エイワ技電

設計

**

製図

**

検図


**

日付

26/06/09

頁

7 / 12

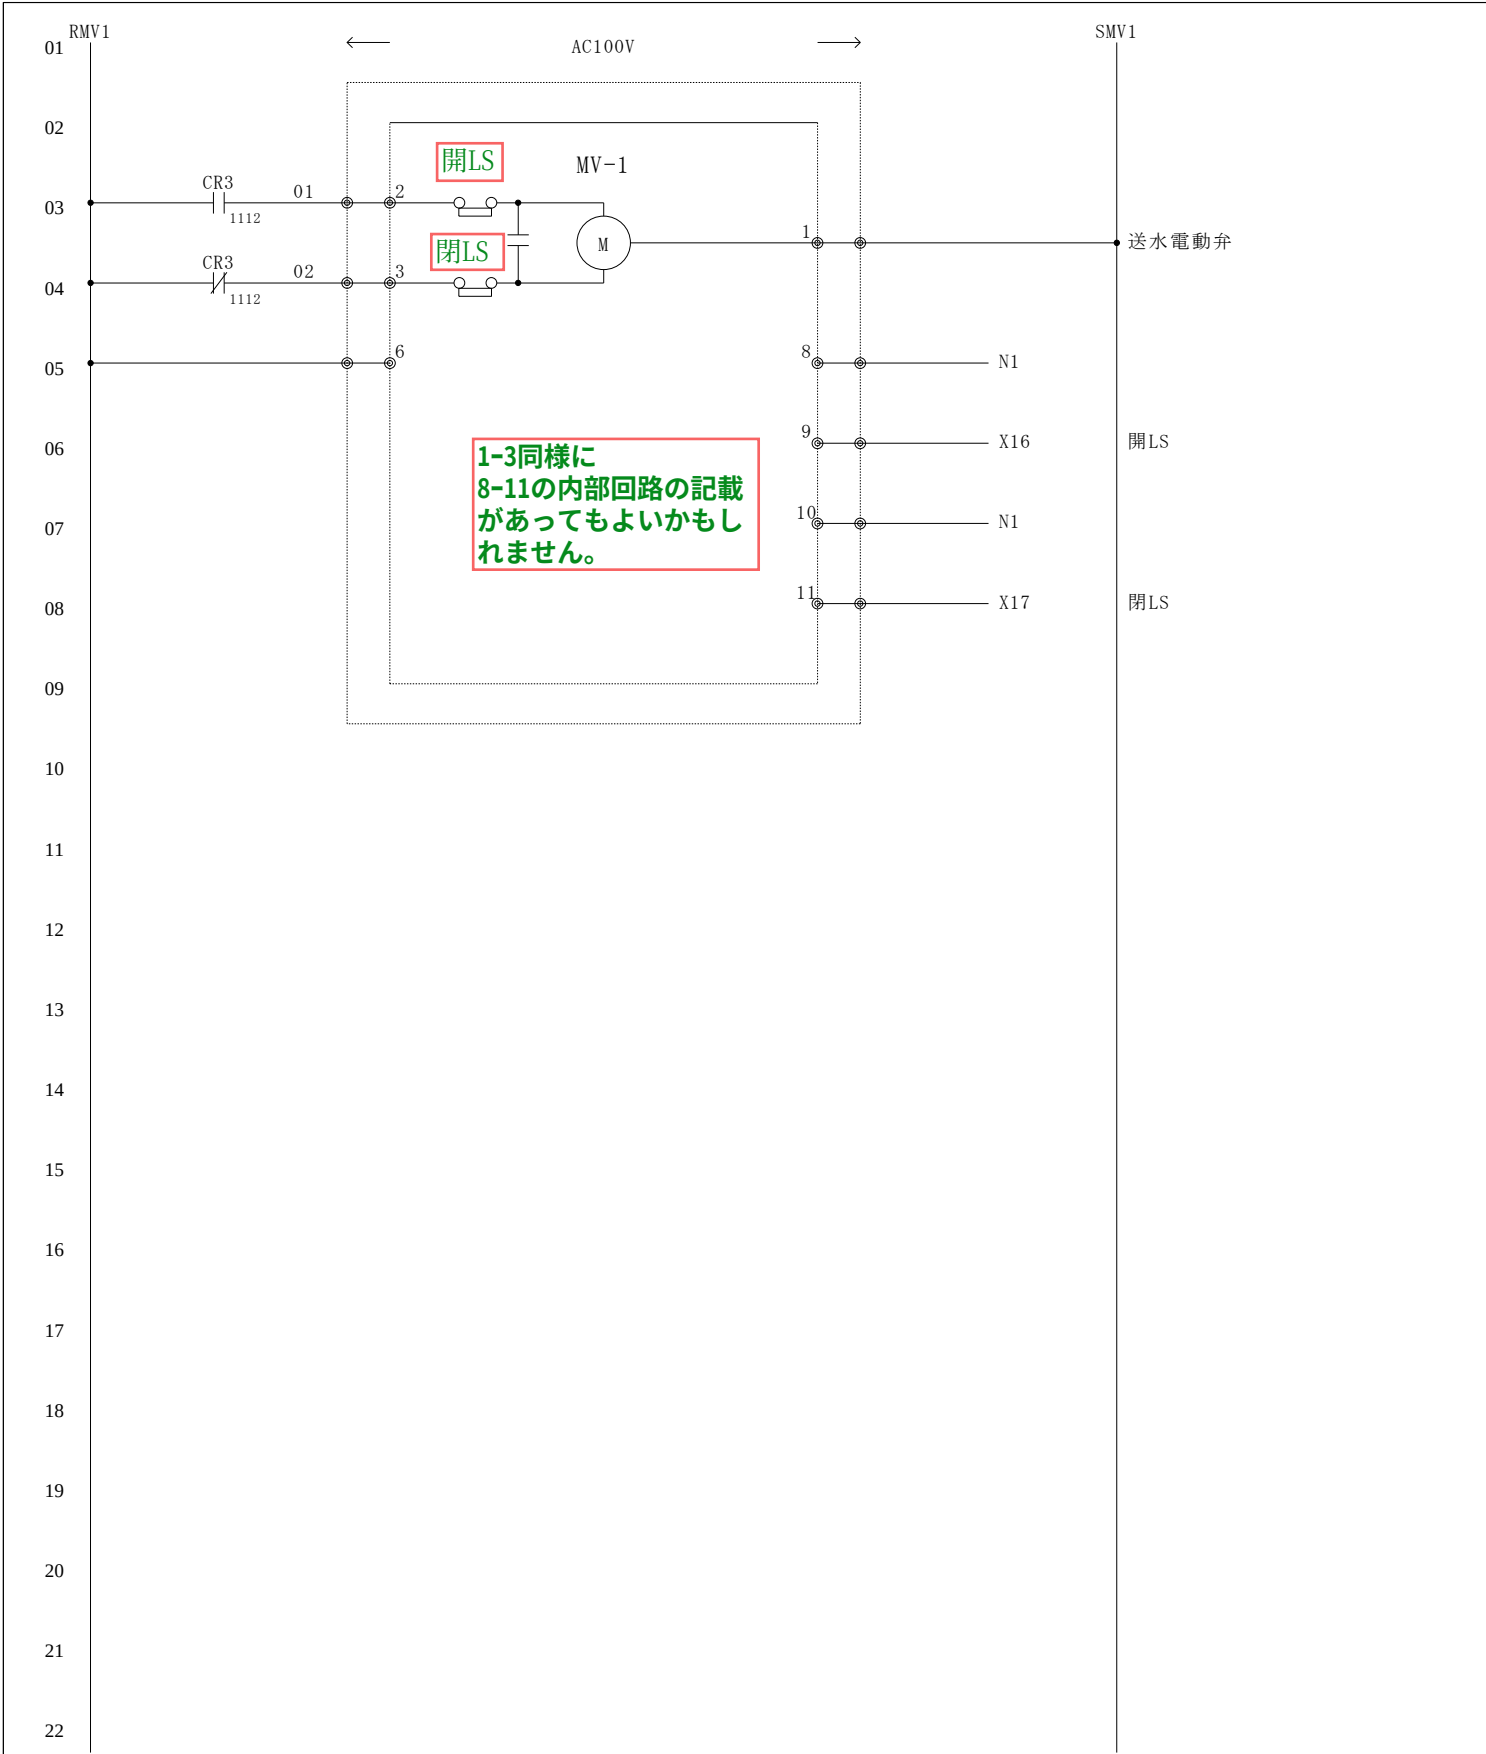

株式会社 アドマテックス美濃

殿

図番名

クーリングタワー制御盤

有限会社 エイワ技電

設計

**

製図

**

検図


**

日付

26/06/09

頁

8 / 12

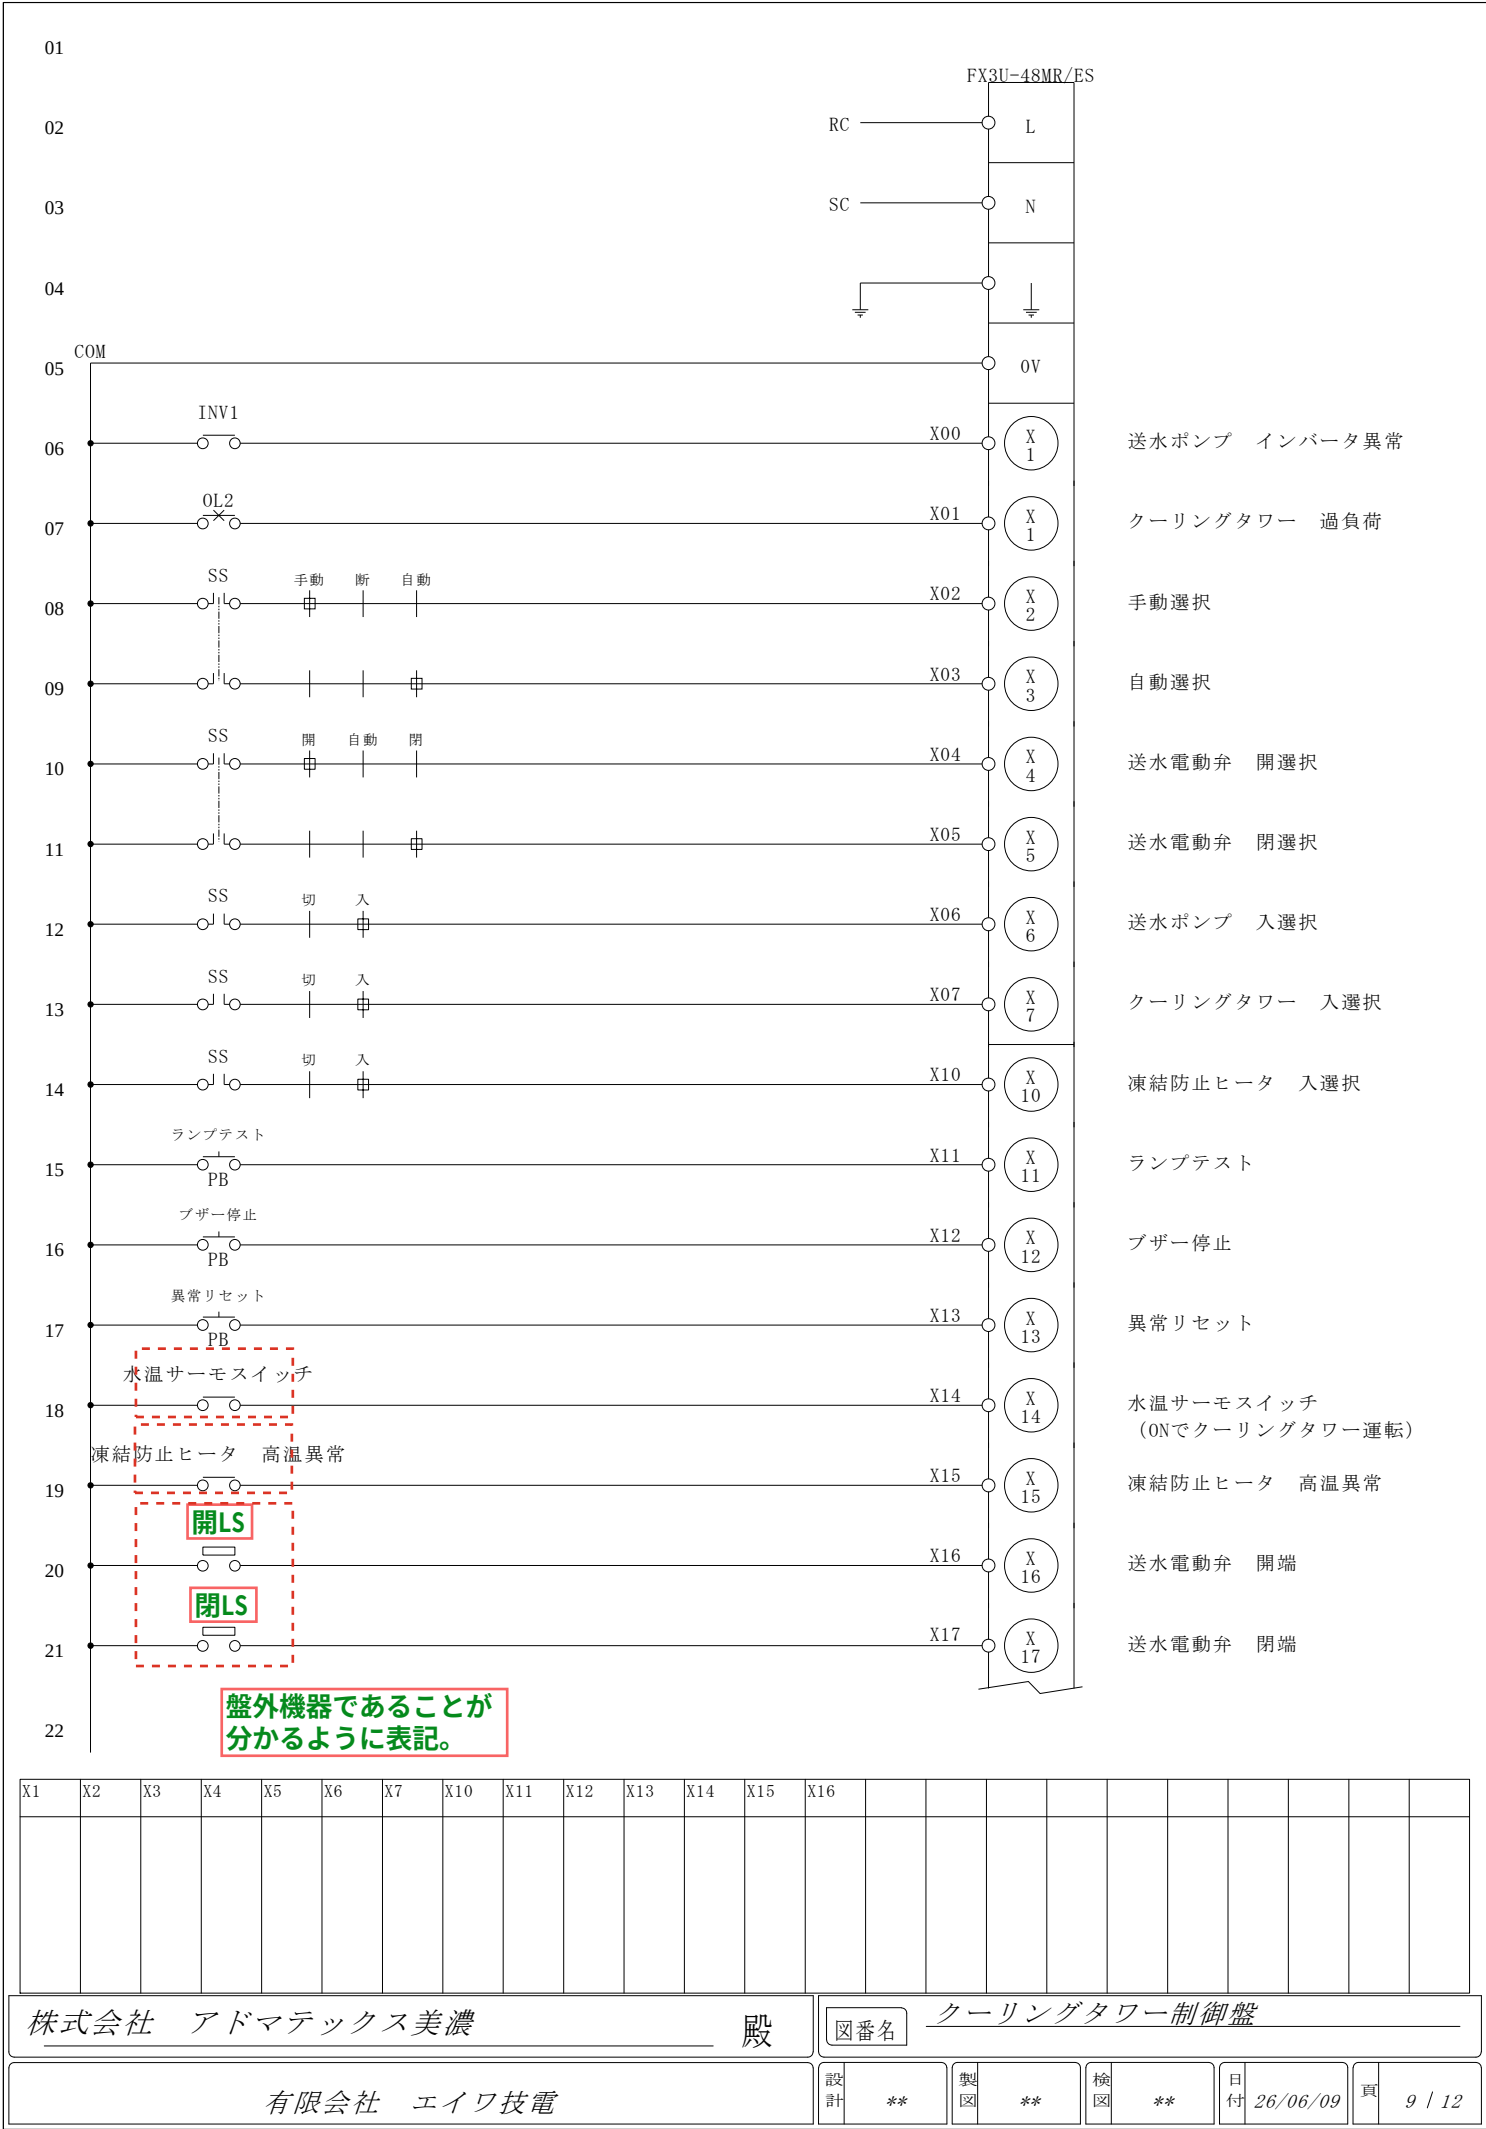

01

FX3U-48MR/ES



10

11

12

13

14

15

10

[illegible]

株式会社 アドマテックス美濃

図番名 クーリングタワー制御盤

有限会社 エイワ技電

設計	**
----	----

製
図
**

検 図	**
--------	----

日付 26/06/09

頁 10 / 12

FX3U-48MR/ES

S/S

24V

COM1

Y0
11Y1
11

Y2

Y3
11

COM2

Y4

Y5

Y6

Y7

COM3

Y10

Y11

Y12

Y13

株式会社 アドマテックス美濃		殿		図番名 クーリングタワー制御盤	
有限会社 エイワ技電		設計 **	製図 **	検図 **	日付 26/06/09
				頁	11 / 12

